
# VEDERE IN PLAN CABINA PUT

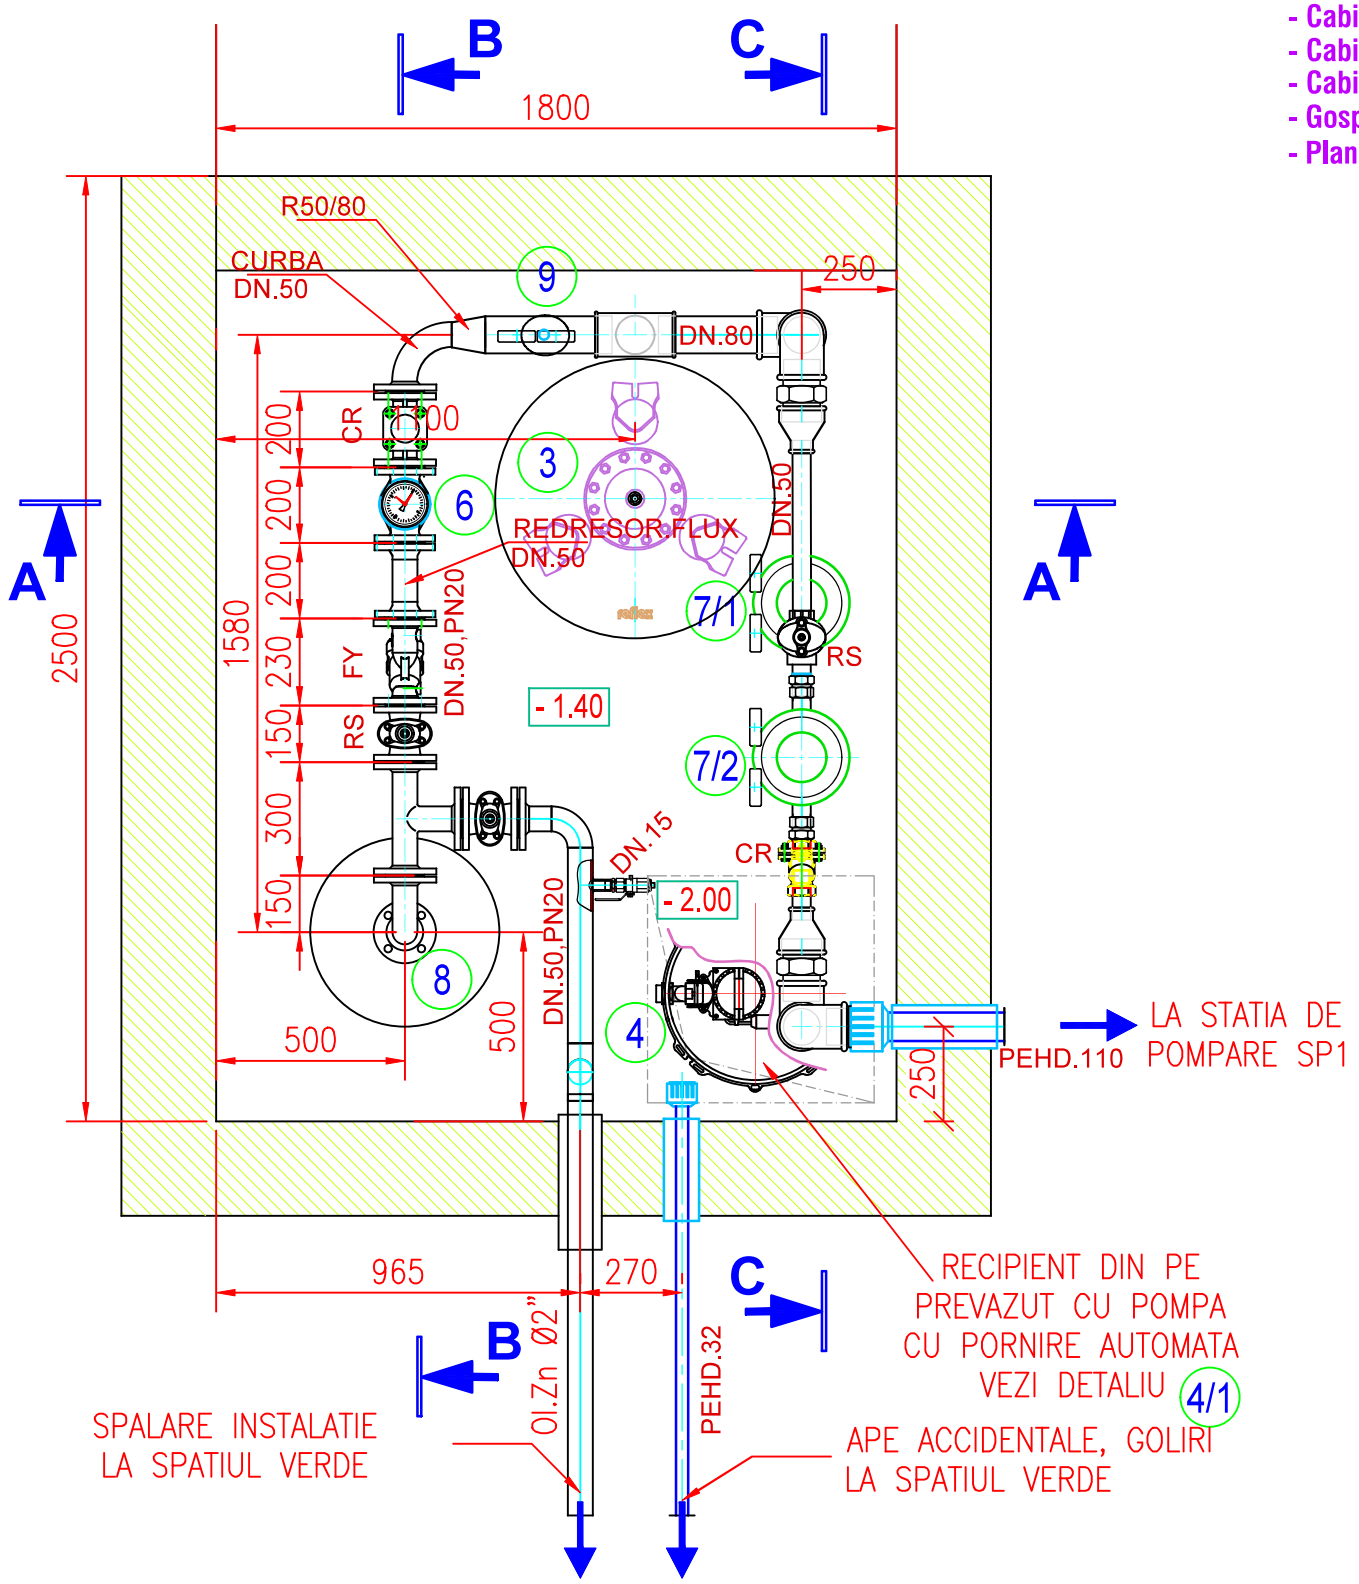


**NOTA:**

**Prezentul plan se consulta cu planurile:**
- **Cabina put - Vedere A-A**
- **Cabina put - Vedere B-B**
- **Cabina put - Vedere C-C**
- **Gospodarie apa - Racorduri rezervor**
- **Plan de amplasare Gospodarie de Apa**

## LISTA DE UTILAJE:

3 - *Vas presiune cu membrana cu trecere directa, PN.25, V=600l*

4 - *Recipient din PE neagra, prevazut cu Pompa de basa cu plutitor, q=2mc/h, P=300W, U=220v, pentru ape cu impuritati reduse, capac din fonta cu sifon pentru ape de pardoseala*


6 - *APOMETRU pentru apa rece, montare in camin, din fonta cu capac de protectie, citire directa, Pn.20, DN.50, montaj cu flanse, tip Voltman*

7 - *Filtru cu ciclon de sedimentare rapida, montat pe refulare pompa de put cu retinere particole peste 100 microni, Pn.20, DN.50, Qmax=4.0 mc/h,*

8 - *POMPA DE PUT (SE RECOMFIRMA DUPA EXECUTARE FORAJ PUT), Qmax=3,60mc/h, H pompa=170mCA*

9 - *PRESOSTAT pentru comanda pompa de put la montat in Cabina putului, comanda oprirea pompei de put la inchiderea de siguranta cu robinetul flotor*

## LEGENDA:

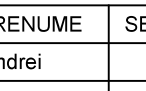


*- ROBINET CU SETAR DIN FONTA, CU MUFE DE LEGATURA, PN-20, ref. AGREMENTATA CE PENTRU APA POTABILA*




*- ROBINET CU SETAR DIN FONTA, CU FLANSE DE LEGATURA, PN-20, AGREMENTATA CE PENTRU APA POTABILA*




*- CLAPETA DE RETINERE CU BILA, CU FLANSE DE LEGATURA, PN-20, AGREMENTATA CE PENTRU APA POTABILA;*



*- CLAPETA DE RETINERE CU BILA, CU MUFE DE LEGATURA, PN-20, AGREMENTATA CE PENTRU APA POTABILA*




*- ROBINET CU CLAPA FLUTURE, MONTAT CU FLANSE, PN-20, referinta AGREMENTATA CE PENTRU APA POTABILA*




*- FILTRU DE RETINERE TIP Y, CU SITA DIN OTEL INOX, CU FLANSE DE LEGARURA SI ROBINET DE SPALARE, AGREMENTATA CE PENTRU APA POTABILA*



*- ROBINET CU SFERA DIN ALAMA, PN-20 referinta Armatura Cluj, sau similar;*




*- ROBINET ANTIVIBRANT, CU FLANSE DE LEGATURA, PN-20, se procura cu pompa hidrofor;*



*- FLASA DIN OTEL PN-20, imbinata prin sudura electrica*

## NOTA:

- In conformitate cu normativul P 100 -1/2013, Clasa de importanta este: III
- Categoria de importanta conform HG 766/21.11.1997 este : C

* CONDUCTELE MONTATE IN GOSP DE APA SI SUNT DIN OTEL ZINCAT, CU IMBINARE PRIN PIESE DE LEGATURA DIN OTEL
CONDUCTELE SE VOR IZOLA CU TUBURI SAU SALTELE DIN POLIURETAN TIP TUBOLIT/ KAIFLEX CU GROSIME DE g = 19 mm
DACA SE UTILIZEAZA IMBINAREA PRIN SUDURA ATUNCI SE VA UTILIZA METODA DE "SUDOBRAZARE" PT.APA POTABILA

* APARATELE DE MASURA SI CONTROL VOR FI PREVAZUTE OBLIGATORIU CU ROBINETI DE INCHIDERE.
DOMENIUL DE MASURARE VA FI : TERMOMETRE 0 - 100°C; MANOMETRE 0 - 20 bari
MARIMEA CADRANULUI VA FI MINIM 80mm , RECOMANDABIL 100mm DIAMETRU.

* COTELE DE NIVEL DIN PREZENTUL PLAN NOTATE CU "CR", REPREZINTA COTA INFERIOARA A CONDUCTELOR

* COTELE DE NIVEL DIN PREZENTUL PLAN NOTATE CU "Cax", REPREZINTA COTA IN AX A CONDUCTELOR

* PENTRU EVENTUALE SITUATII DE NECOORDONARE A TRASEELOR CU CELELALTE TIPURI DE INSTALATII
SE VA SESIZA PROIECTANTUL DE SPECIALITATE INAINTE DE EXECUTAREA LUCRARILOR,
URMAND CA CEI IMPLICATI SA STABILEASCA SOLUTIILE DE MODIFICARE CONFORM NORMELOR IN VIGOARE


S.C. INTERACTIVE DESIGN S.R.L.
Adresa: Str. Mihai Eminescu, Nr. 171, Sector 2, Bucuresti
J39/451/14.06.2006, C.I.F. : RO 18766818,
Tel: 0724.100.450 : Fax: 031.817.22.89
office@interactive-design.ro


Beneficiar : Comuna Saschiz
Adresa : sat Saschiz, comuna Saschiz, judeţul Mureş

Denumire Proiect : "EXTINDEREA ŞI MODERNIZAREA SISTEMULUI DE ALIMENTARE CU APĂ DIN COMUNA SASCHIZ, JUDEŢUL MUREŞ"

| SPECIFICATIE | NUME SI PRENUME | SEMNATURA |
|---|---|---|
| SEF PROIECT | ing. Tudor Andrei | |
| PROIECTAT | ing. Tudora Cristian | |
| DESENAT | ing. Tudora Cristian | |
| VERIFICAT | ing. Dragne Mihai | |

Proiect nr : ID 315 / 10.2019 — Data : 10.2019
Specialitatea : Hidroedilitare — Faza : P.A.C. D.T.O.E. P.T.
Denumire Plansa : Gospodaria de Apa, Sat Saschiz — Cabina put F1 - VEDERE IN PLAN — Scara : 1:20
Nr : DT.07


Proprietatea intelectuala a S.C. INTERACTIVE DESIGN S.R.L.
Orice multiplicare sau modificare adusa proiectului nu poate fi realizata fara acordul firmei