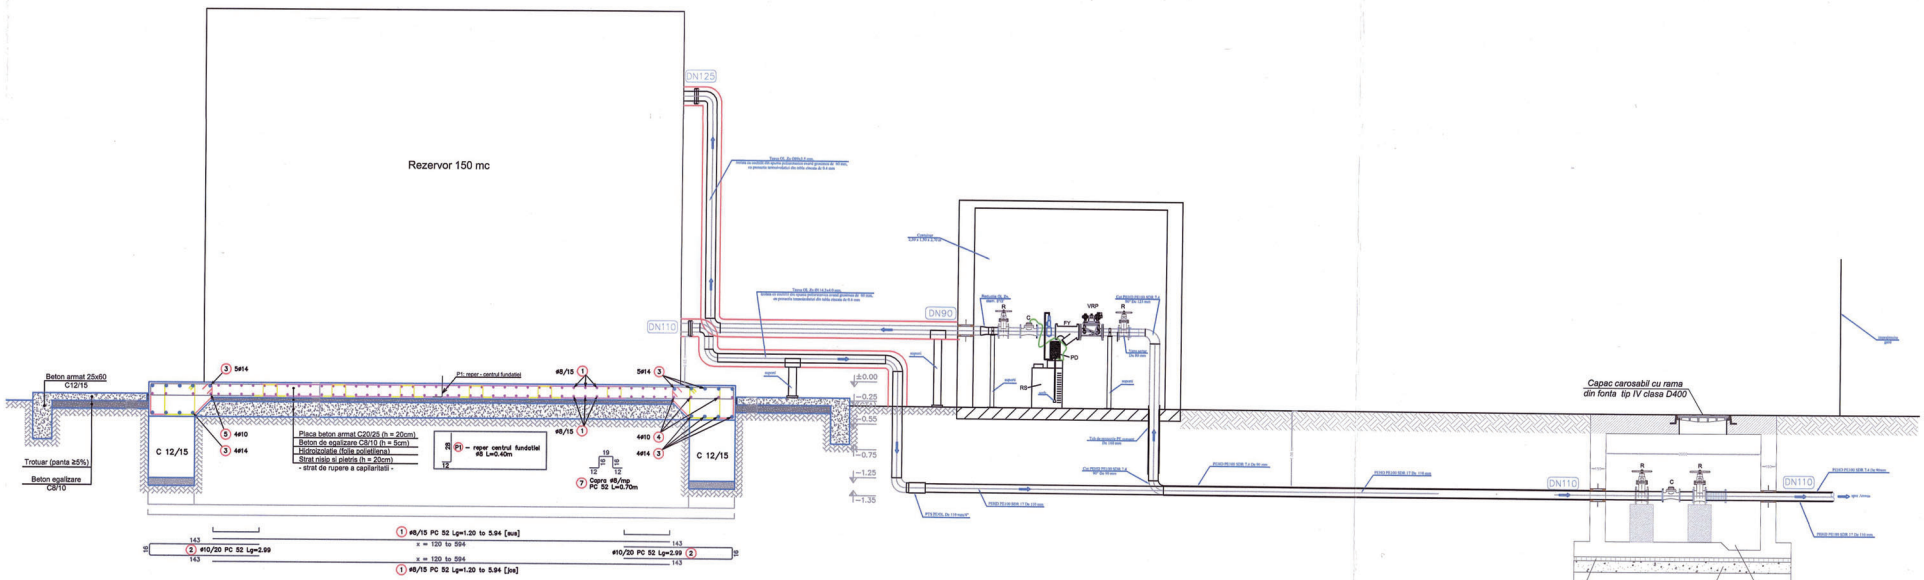



LEGENDĂ :

PD - pompa dozatoare cu membrana, protectie IP 65, carcasa din plastic, alimentare electrica 230V a.c. 50 Hz
FY - filtru imputitati tip Y, corp din fonta, cu flanse
RS - recipient de stocare a solutiei de hipoclorit, realizat din polietilena rezistenta la actiunea agentilor chimici, avand capacitatea de 50 L, diam. 400 mm
TC - Tablou de comanda și protectie
R - robinet de inchidere cu sertar Pn 25 bar
VRP - vana reducere presiune Dn 80 mm
C - contor apa

Revizie/ Revision				Aprobat/Approved	Data/Date
0	Denumire/Description				
Verificatori/ Experti	Nume/Names	Cerinta/ Specialty	Semnatura/ Signature	Referat verificare proiect/Expertiza nr./data Technical Assessment no./date	
Verifiers/ Experts					

Proiectant de specialitate /Specialized Designer
S.C. MONTREPCOM S.R.L.
com. Ungheni, satul Reciaș, județul Sibiu/ Reciș RO
J26/1530/1991-R1220985
office@montrepcom.ro
tel/fax:+40.265.254.209; 0730808101

Specificatie/ Position	Nume/Names	Semn/Sign	Scara/Scale	Beneficiar/ Customer	Nr. proiect:/ Design no
Sef proiect/ Project leader	ing. Varga Daniel		1:50	ORAȘUL SĂLIȘTE loc. Saliste, str. Steaza, nr. 9, jud. Sibiu	09-AP/2024
Proiectat/ Designed	ing. Balazs Nandor		Data/Date 2025	Denumire lucrare/ Project name: Alimentare cu apa în loc. Amnas si conducta de aductiune pentru asigurarea apei potabile in sistemul de alimentare a localitătii Aciliu, oras Saliste, jud. Sibiu	Faza/Phase P.T.+D.E.
Desenat/ Drawn	ing. Dumitru Silviu			Denumire plansa/Drawing Title: Statia dozare cu hipoclorit de sodiu, camin vane CV	Nr. Plansa S21

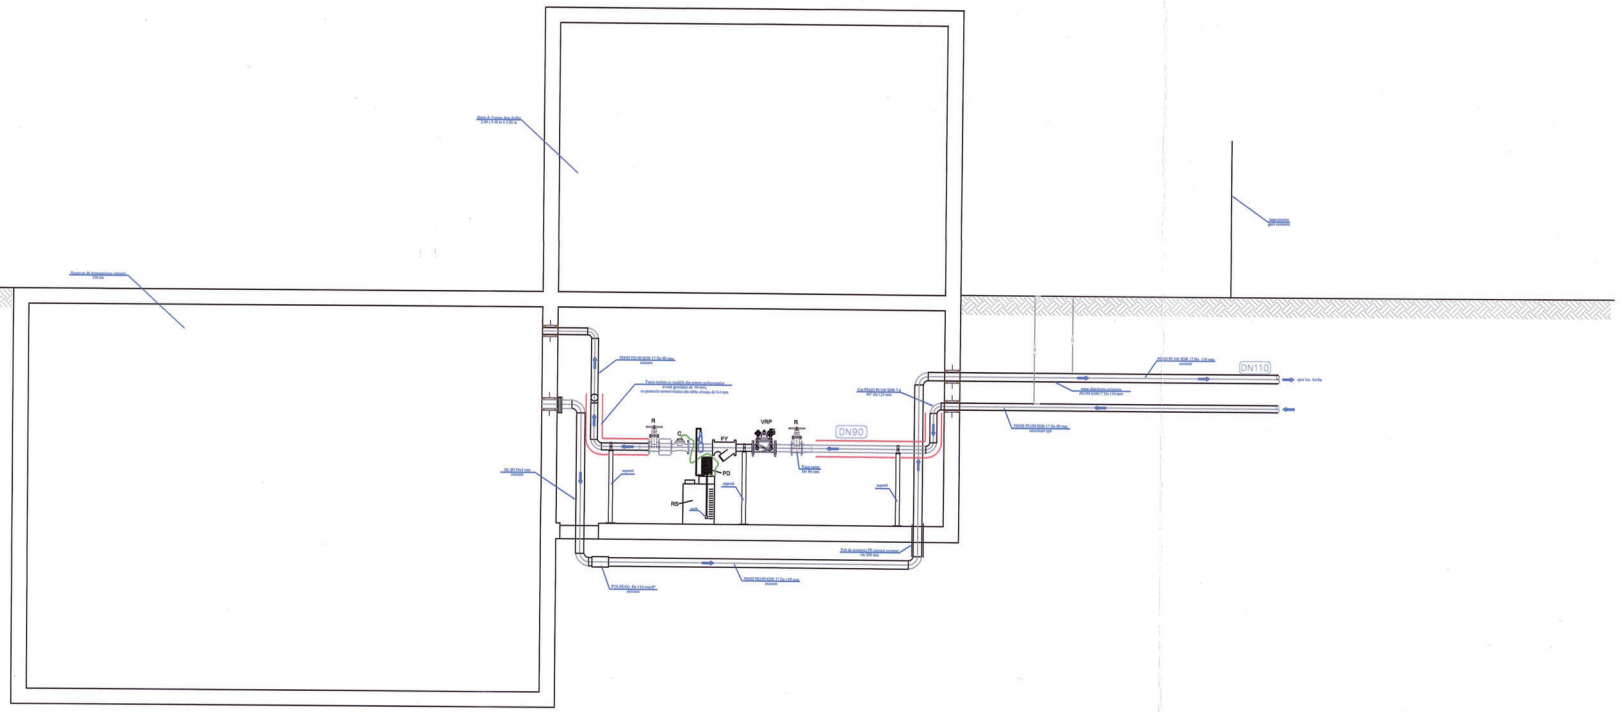

LEGENDĂ :

PD - pompa dozatoare cu membrana, protectie IP 65, carcasa din plastic, alimentare electrica 230V a.c. 50 Hz
FY - filtru imputitati tip Y, corp din fonta, cu flanse
RS - recipient de stocare a solutiei de hipoclorit, realizat din polietilena rezistenta la actiunea agentilor chimic, avand capacitatea de 50 L, diam. 400 mm
TC - Tablou de comanda şi protectie
R - robinet de inchidere cu sertar Pn 25 bar
VRP - ventil reductor presiune Dn 80 mm, Pn 16 bar
C - contor apa

Revizie/ Revision					Aprobat/Approved	Data/Date
0		Denumire/Description				
Verificatori/ Experti	Nume/Names	Centra/ Speciality	Semnatura/ Signature	Referat verificare proiect/Expertiza nr./data Technical Assessment no./date		
Verifiers/ Experts						

Proiectant de specialitate /Specialized Designer S.C. MONTREPCOM S.R.L. com. Urghers, satul Recea, popasul Izvorul Rece-RO J26/1530/1991-R1220085 office@montrepcom.ro tel/fax:+40.265.254.209; 0730808101				Beneficiar/ Customer **ORAŞUL SĂLIŞTE** **loc. Saliste, str. Steaza, nr. 9, jud. Sibiu**	Nr. proiect:/ Design no 09-AP/2024
Specificatie/ Position	Nume/Names	Semn/Sign	Scara/Scale 1:50	Denumire lucrare/ Project name **Alimentare cu apa in loc. Amnas si conducta de aductiune pentru asigurarea apei potabile in sistemul de alimentare a localitatii Aciliu, oras Saliste, jud. Sibiu**	**Faza/Phase** *P.T.+D.E.*
Sef proiect/ Project leader	ing. Varga Daniel				
Proiectat/ Designed	ing. Balazs Nandor		Data/Date 2025	Denumire plansa/Drawing Title: Statia dozare cu hipoclorit de sodiu, loc. Aciliu	Nr. Plansa *S22*
Desenat/ Drawn	ing. Dumitru Silviu				