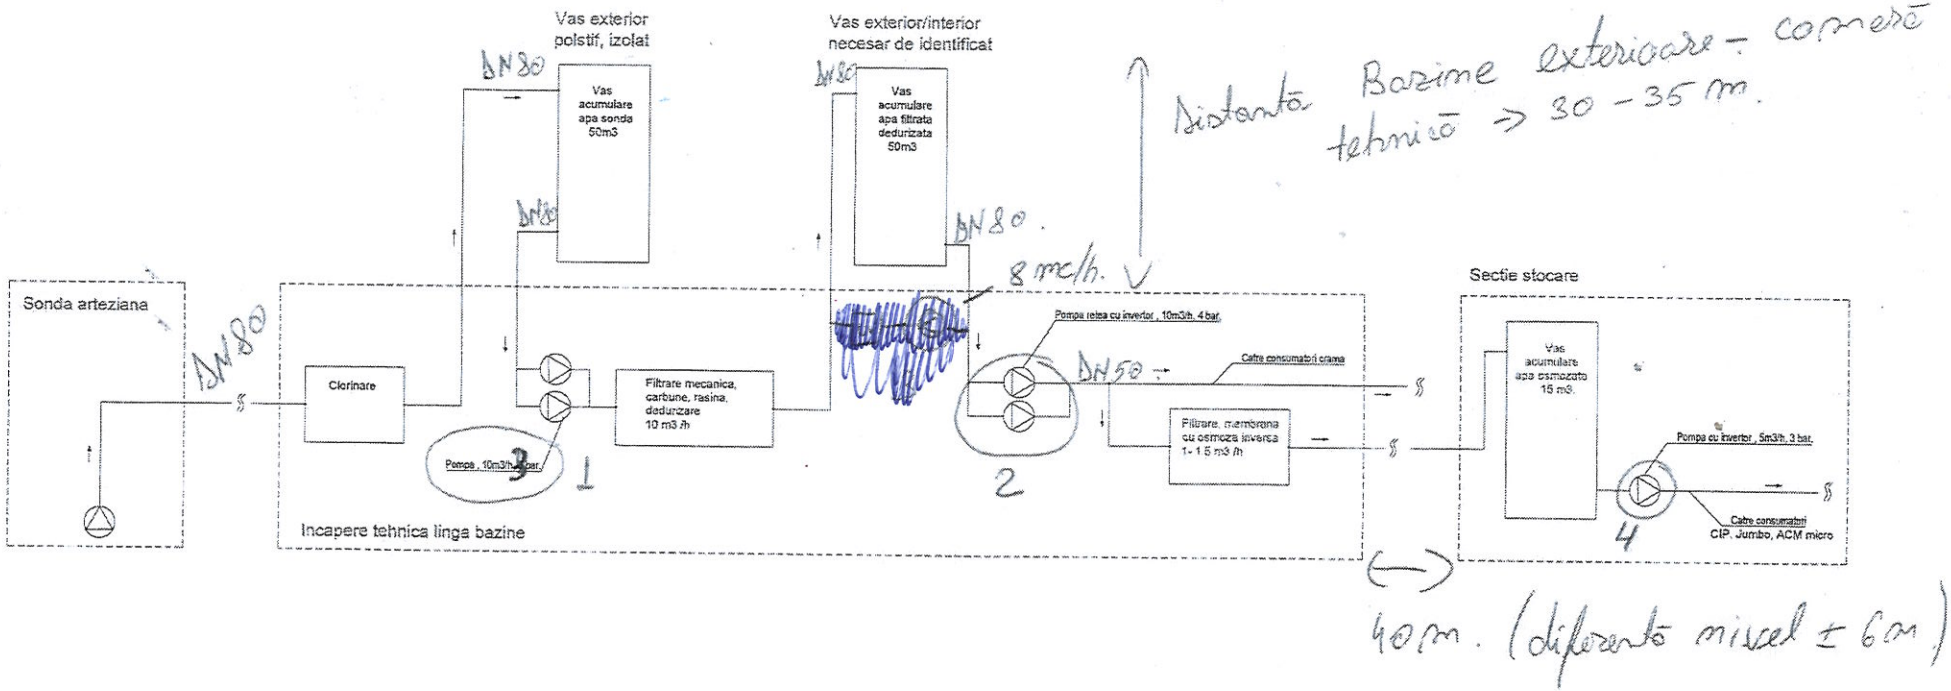

Vas exterior polstif, izolat
DN80
Vas acumulare apa sonda 50m3
Vas exterior/interior necesar de identificat
DN80
Vas acumulare apa filtrata dedurizata 50m3
DN80
DN80
8 mc/h.
Distanta Bazine exterioare - cameră tehnică → 30 - 35 m.
Sonda arteziana
DN80
Clorinare
Pompa , 10m3/h, 3 bar
3
1
Filtrare mecanica, carbune, rasina, dedurizare 10 m3 /h
Incapere tehnica linga bazine
Pompa relea cu invertor , 10m3/h, 4 bar
DN50
Catre consumatorii crama
Filtrare membrana cu osmoza inversa 1- 1.5 m3 /h
2
Sectie stocare
Vas acumulare apa osmozata 15 m3.
Pompa cu invertor , 5m3/h, 3 bar
Catre consumatori CIP, Jumbo, ACM micro
4
40m. (diferenta nivel ± 6m)