

SCHEMA FUNCTIONALA GOSPODARIE DE APA RECE

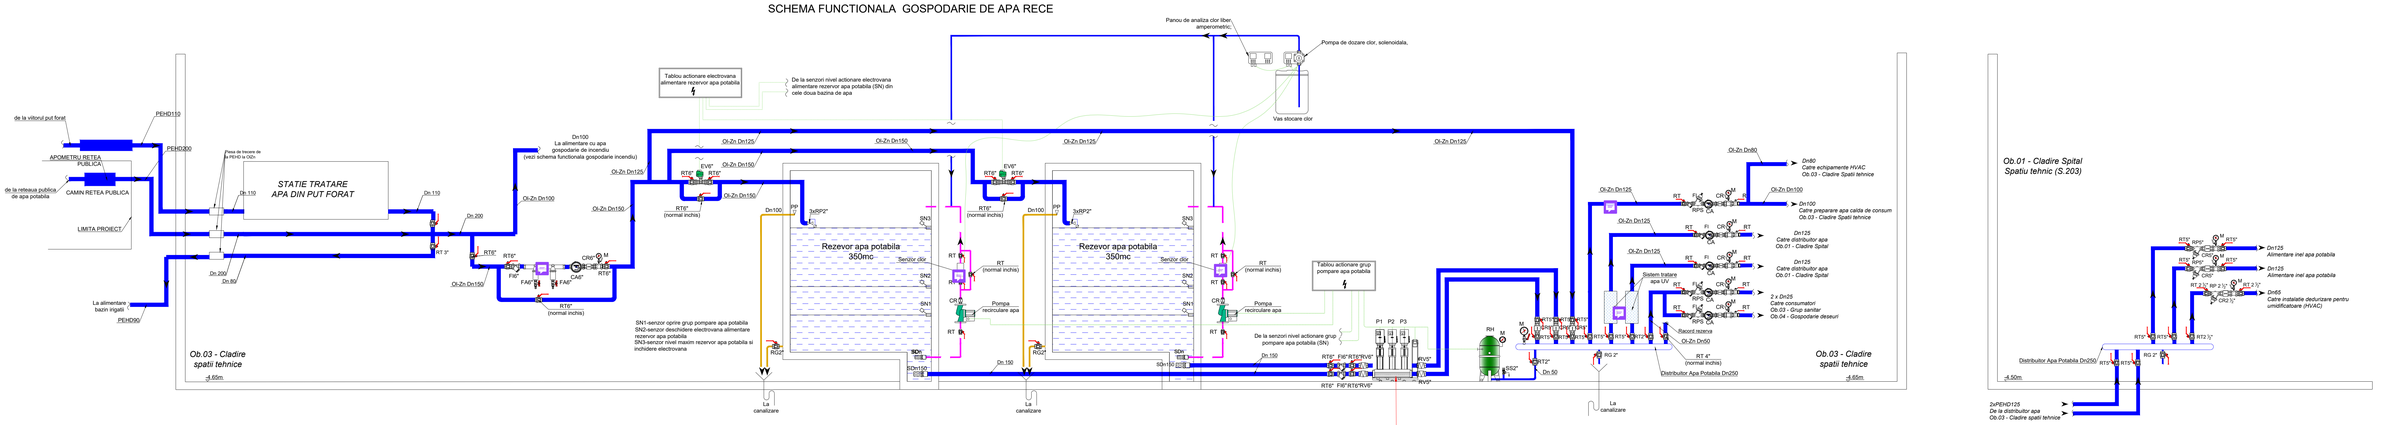

Grup electropompe pentru apa menajera 3 buc (2F+1R) cu turatie variabila
P1 pompa baza (F) Q = xx mc/h; H=70 mCA;
P2 pompa baza (F) Q = xx mc/h; H=70 mCA;
P3 pompa rezerva (R) Q = xx mc/h; H=70 mCA;
Functionare grup pompare apa menajera
Pompa baza/rezerva
Presiune pornire: -20mCA din Hnec;
Presiune oprire: +10 mCA fata de Hnec;

SN1-senzor oprire grup pompare apa potabila
SN2-senzor deschidere electrovana alimentare rezervor apa potabila
SN3-senzor nivel maxim rezervor apa potabila si inchidere electrovana


SCHEMA SENZORI ACTIONARE ELECTROVANA ALIMENTARE REZERVOR APA POTABILA

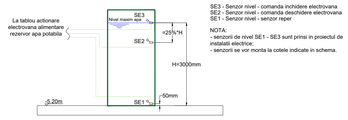

SE3 - Senzor nivel - comanda inchidere electrovana
SE2 - Senzor nivel - comanda deschidere electrovana
SE1 - Senzor nivel - senzor reper

NOTA:
- senzorii de nivel SE1 - SE3 sunt prinsi in proiectul de instalatii electrice;
- senzorii se vor monta la cotele indicate in schema.

SCHEMA SENZORI ACTIONARE POMPE APA POTABILA

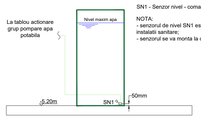

SN1 - Senzor nivel - comanda oprire pompe (lipsa apa)

NOTA:
- senzorul de nivel SN1 este prins in proiectul de instalatii sanitare;
- senzorul se va monta la cota indicata in schema.

LEGENDA

	CONDUCTA APA RECE PENTRU UZ MENAJER;
	CONDUCTA RECIRCULARE APA BAZIN;
	CONDUCTA GOLIRE;
	CIRCUIT ELECTRIC;
Fi	FILTRU DE IMPURITATI;
RT	ROBINET DE TRECERE;
CR	CLAPETA DE RETINERE CU CLAPA;
CA	CONTOR APA CU TRANSMITERE LA DISTANTA;
RH	RECIPIENT HIDROFOR;
SN	SENZOR NIVEL;
SB	SORB CU SITE PENTRU ASPIRATIE POMPE;
PP	PREA PLIN;
FA	FILTRU CU AUTOCURATARE DIN OTEL CARBON;
SS	SUPAPA DE SIGURANTA;
RV	RACORD ANTIVIBRANT;
RP	ROBINET CU PLUTITOR;
EV	ELECTROVANA CU ARC CU REVENIRE;
M	MANOMETRU VERIFICARE PRESIUNE;
RG	ROBINET GOLIRE;
RV	RACORD ELASTIC ANTIVIBRANT;
RPS	REDUCTOR DE PRESIUNE;

NOTA:
Aceasta plansa nu poate fi folosit a pentru construire inainte de obtinerea autorizatiei de construire.
Orice neconcordanta constatata se va semnala proiectantului.
Toate dimensiunile se vor verifica in santier inainte de executarea lucrarilor.
A nu se scala dupa desen.

Categoria de importanta :	**C (normala)**
Clasa de importanta:	**III, cf. P100-1/2013**
Nivel de stabilitate la incendiu :	**II, cf. P118-1/2025**
Categorie de pericol de incendiu:	**-**
Risc de incendiu:	**mic**

±0.00 = +541.95

Rev.	Descriere	Data	Intocmit

ANTREPRENOR GENERAL:
SC UBITECH CONSTRUCTII SRL
J2019013056405

PROIECTANT GENERAL:
SC LEVIATAN DESIGN S.R.L.
J2012007016407

NUME PROIECT:	**CONSTRUIRE SPITAL CLINIC DE PNEUMOFTIZIOLOGIE ȘI BOLI INFECȚIOASE BRASOV** **Amplasament: Strada Institutului, nr. 38, Municipiul Bra sov, Judetul Brasov**		
BENEFICIAR:	**PRIMARIA MUNICIPIULUI BRASOV** **Adresa:** B-dul. Eroilor nr 8, Municipiul Brasov, Judetul Brasov		
SPECIALITATEA:	**INSTALATII SANITARE**	FAZA: **P.Th. - D.D.E.**	
DENUMIRE PLANSA:	**OB03 - Cladire Spatii Tehnice** Schema functionala gospodarie apa potabila	Nr. Contract: **244/118774/ 29.07.2025**	Nr. Proiect: **0040325**
Sef Proiect	Arh. Beatrice BALUTA SICLITARU	Scara: **N/A**	Format: A1
Proiectat	Ing. Laura OITA	Data: **OCT.2026**	Revizia: Rev.00
Desenat	Ing. Laura OITA	Codproiect_Plansa: **0040325_IS_Ob.03-100**	
Coordonat	Ing. Corina BACANU		

Acest document este proprietatea SC LEVIATAN DESIGN SRL si nu este permis a reproducerea sa si nici comunicarea cu tinutului s-au fara autorizarea noastra scrisa. Vom solicita protectia legii impotriva oric arui abuz.

A1 594 x 841mm